


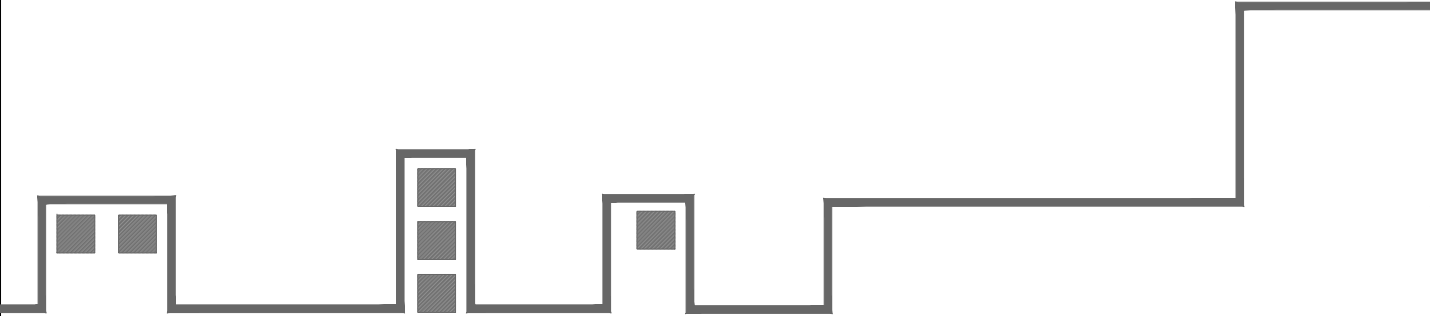

阳光城檀映6#401雅居

室内装饰设计施工图

2021. 03. 25 第二版


建筑				电气		
结构				暖通		
卫生						

阳光城檀映6#401雅居施工图

图 纸 目 录

序号	图 纸 内 容	图 号	序号	图 纸 内 容	图 号	序号	图 纸 内 容	图 号
01	封面		22	玄关、客厅A立面图	LM-01	43		
02	图纸目录	总-1	23	客厅、厨房、餐厅、D立面图	LM-02	44		
03	进场、砌墙、防水，铺砖施工要求	总-2	24	厨房、餐厅B立面图	LM-03	45		
04	电施说明、水电施工标准	总-3	25	客厅B立面图	LM-04	46		
05	木作及油漆施工要求	总-4	26	次卧一D立面图 次卧一A立面图	LM-05	47		
06	原始结构图	PM-01	27	次卧一B立面图 次卧一C立面图	LM-06	48		
07	平面布置图	PM-02	28	干区D立面图 干区B立面图	LM-07	49		
08	拆除示意图	PM-03	29	干区A立面图 公卫A立面图 公卫C立面图	LM-08	50		
09	新建墙体图	PM-04	30	书房B立面图 书房C立面图	LM-09	51		
10	地面材质图	PM-05	31	书房D立面图 书房A立面图	LM-10	52		
11	吊顶布置图	PM-06	32	次卧二A立面图 次卧二B立面图	LM-11	53		
12	吊顶定位图	PM-07	33	次卧二C立面图 次卧二D立面图	LM-12	54		
13	灯具定位图	PM-08	34	主卧A立面图 主卧干区、主卧D立面图	LM-13	55		
14	强弱电布置图	PM-09	35	主卧D立面图 主卧C立面图	LM-14	56		
15	开关控制图	PM-10	36	主卧、主卧干区B立面图	LM-15	57		
16	给水布置图	PM-11	37	主卧干区A立面图 主卫A立面图	LM-16	58		
17	排水布置图	PM-12	38	主卫B立面图 主卫C立面图	LM-17	59		
18	家具尺寸图	PM-13	39			60		
19	立面索引图	PM-14	40			61		
20			41			62		
21			42			63		

单位名称:		
 艾科装饰 Aike Decoration		
备 注:		
施工图审查批准单位:		
施工图审查批准证书号:		
图纸专用章:		
注册建筑师执业章:		
注册工程师执业章:		
工程名称:		
阳光城檀映6#401雅居施工图		
建设单位:		
审 定	董隍	
工程负责人	??	
专业负责人	??	
审 核	??	
校 对	??	
设 计	??	
制 图	?松生	
图 名:		
图纸目录		
工程编号		
图 别	装 施	
图 号	总-01	
日 期	2021/02	

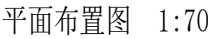

备 注

施工图审查批准单位:

施工图审查批准书证号:

图纸专用章:

注册建筑师执业章:

注册工程师执业章:

工程名称:

福州·阳光城檀映6#401
室内装饰设计施工图

建设单位:

审 定		
工程负责人		
专业负责人		
审 核		
校 对		
设 计		
制 图		

圖	名
---	---

平面布置图

工程编号	
图 别	装 施
图 号	PM-02
日 期	2026/5




福州·阳光城檀映6#401
室内装饰设计施工图

审 定		
工程负责人		
专业负责人		
审 核		
校 对		
设 计		
制 图		

新建墙体图

工程编号	
图 别	装 施
图 号	PM-04
日 期	2026/5

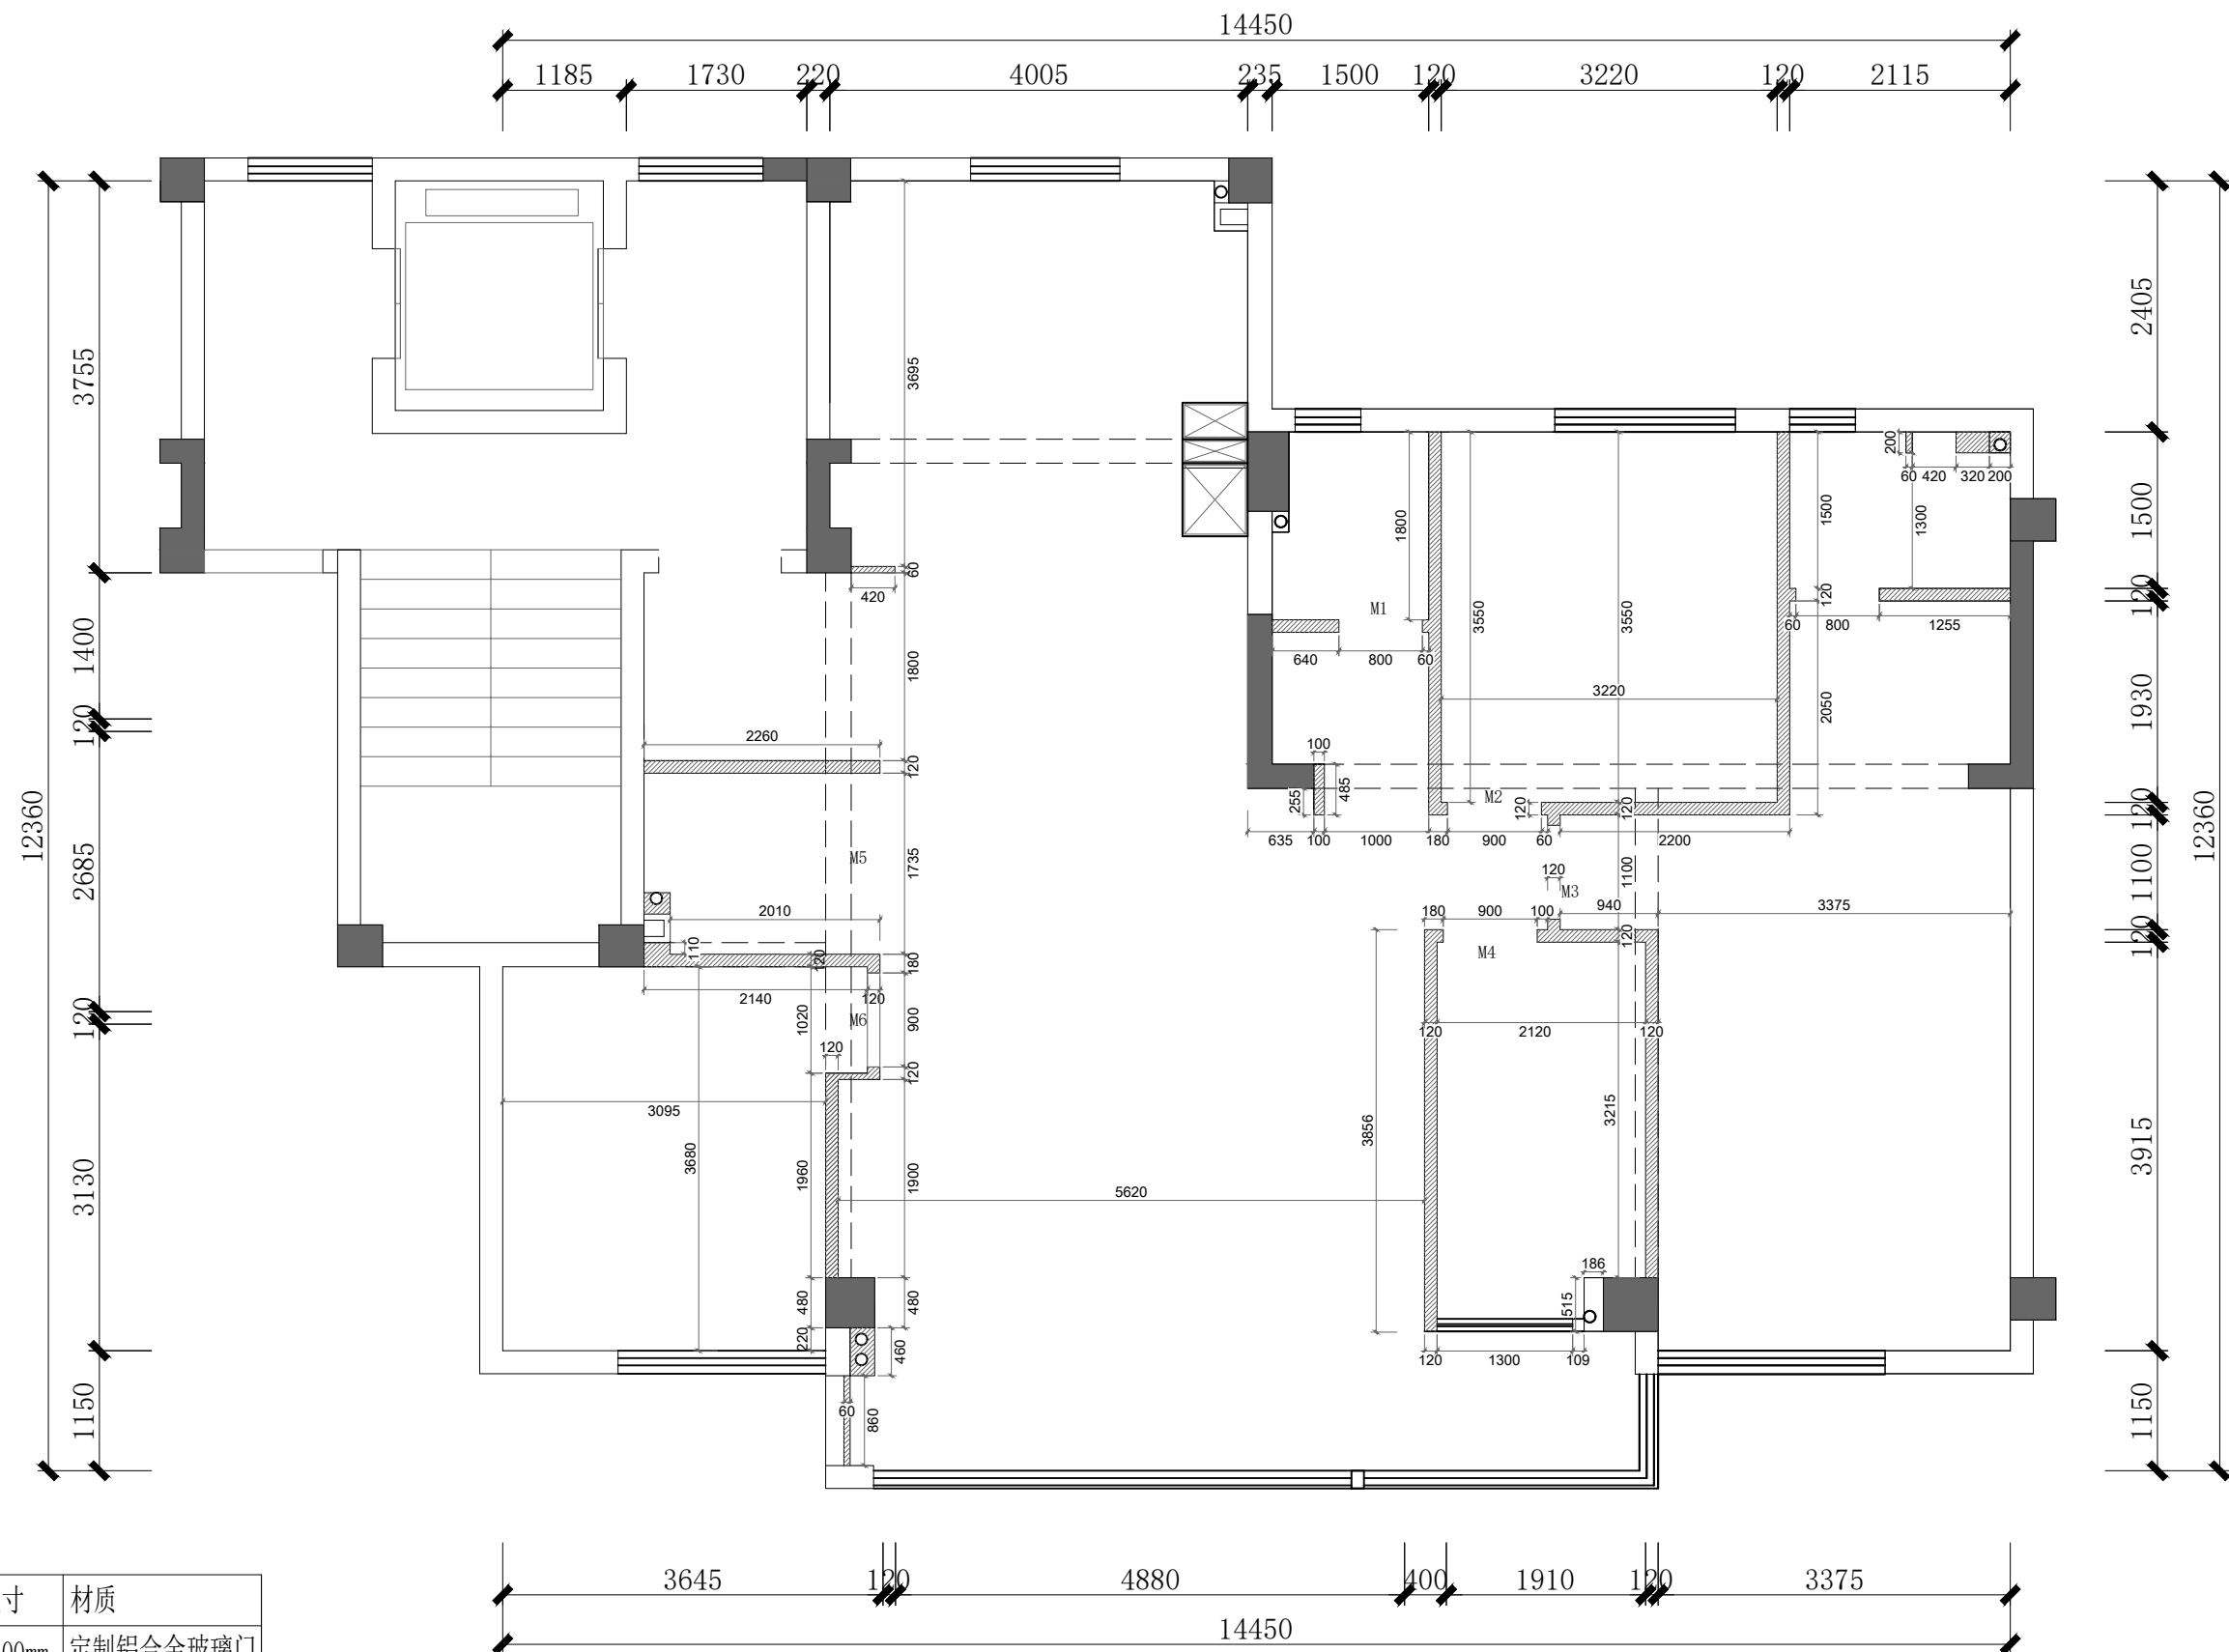

编号	门洞尺寸	材质
M1	800*2400mm	定制铝合金玻璃门
M2	900*2400mm	定制木门
M3	900*2400mm	定制木门
M4	900*2400mm	定制木门
M5	1735*2400mm	八百库柜体门
M6	900*2400mm	定制木门

- | | | |
|---|--------|--|
|  | 柱体或承重墙 | 1. 卫生间、厨房新建的墙体砌墙前须先浇筑混凝土防水地梁。 |
|  | 原有砖墙体 | 2. 除有特殊标注外所有新砌墙体均砌为100mm实心黏土砖，所有包管做隔音处理。 |
|  | 新砌墙体 | 3. 原外建筑窗根据业主实际需要进行更换。 |

新建墙体图 1:50




福州·阳光城檀映6#401
室内装饰设计施工图

2. 2.

日 月

026/5

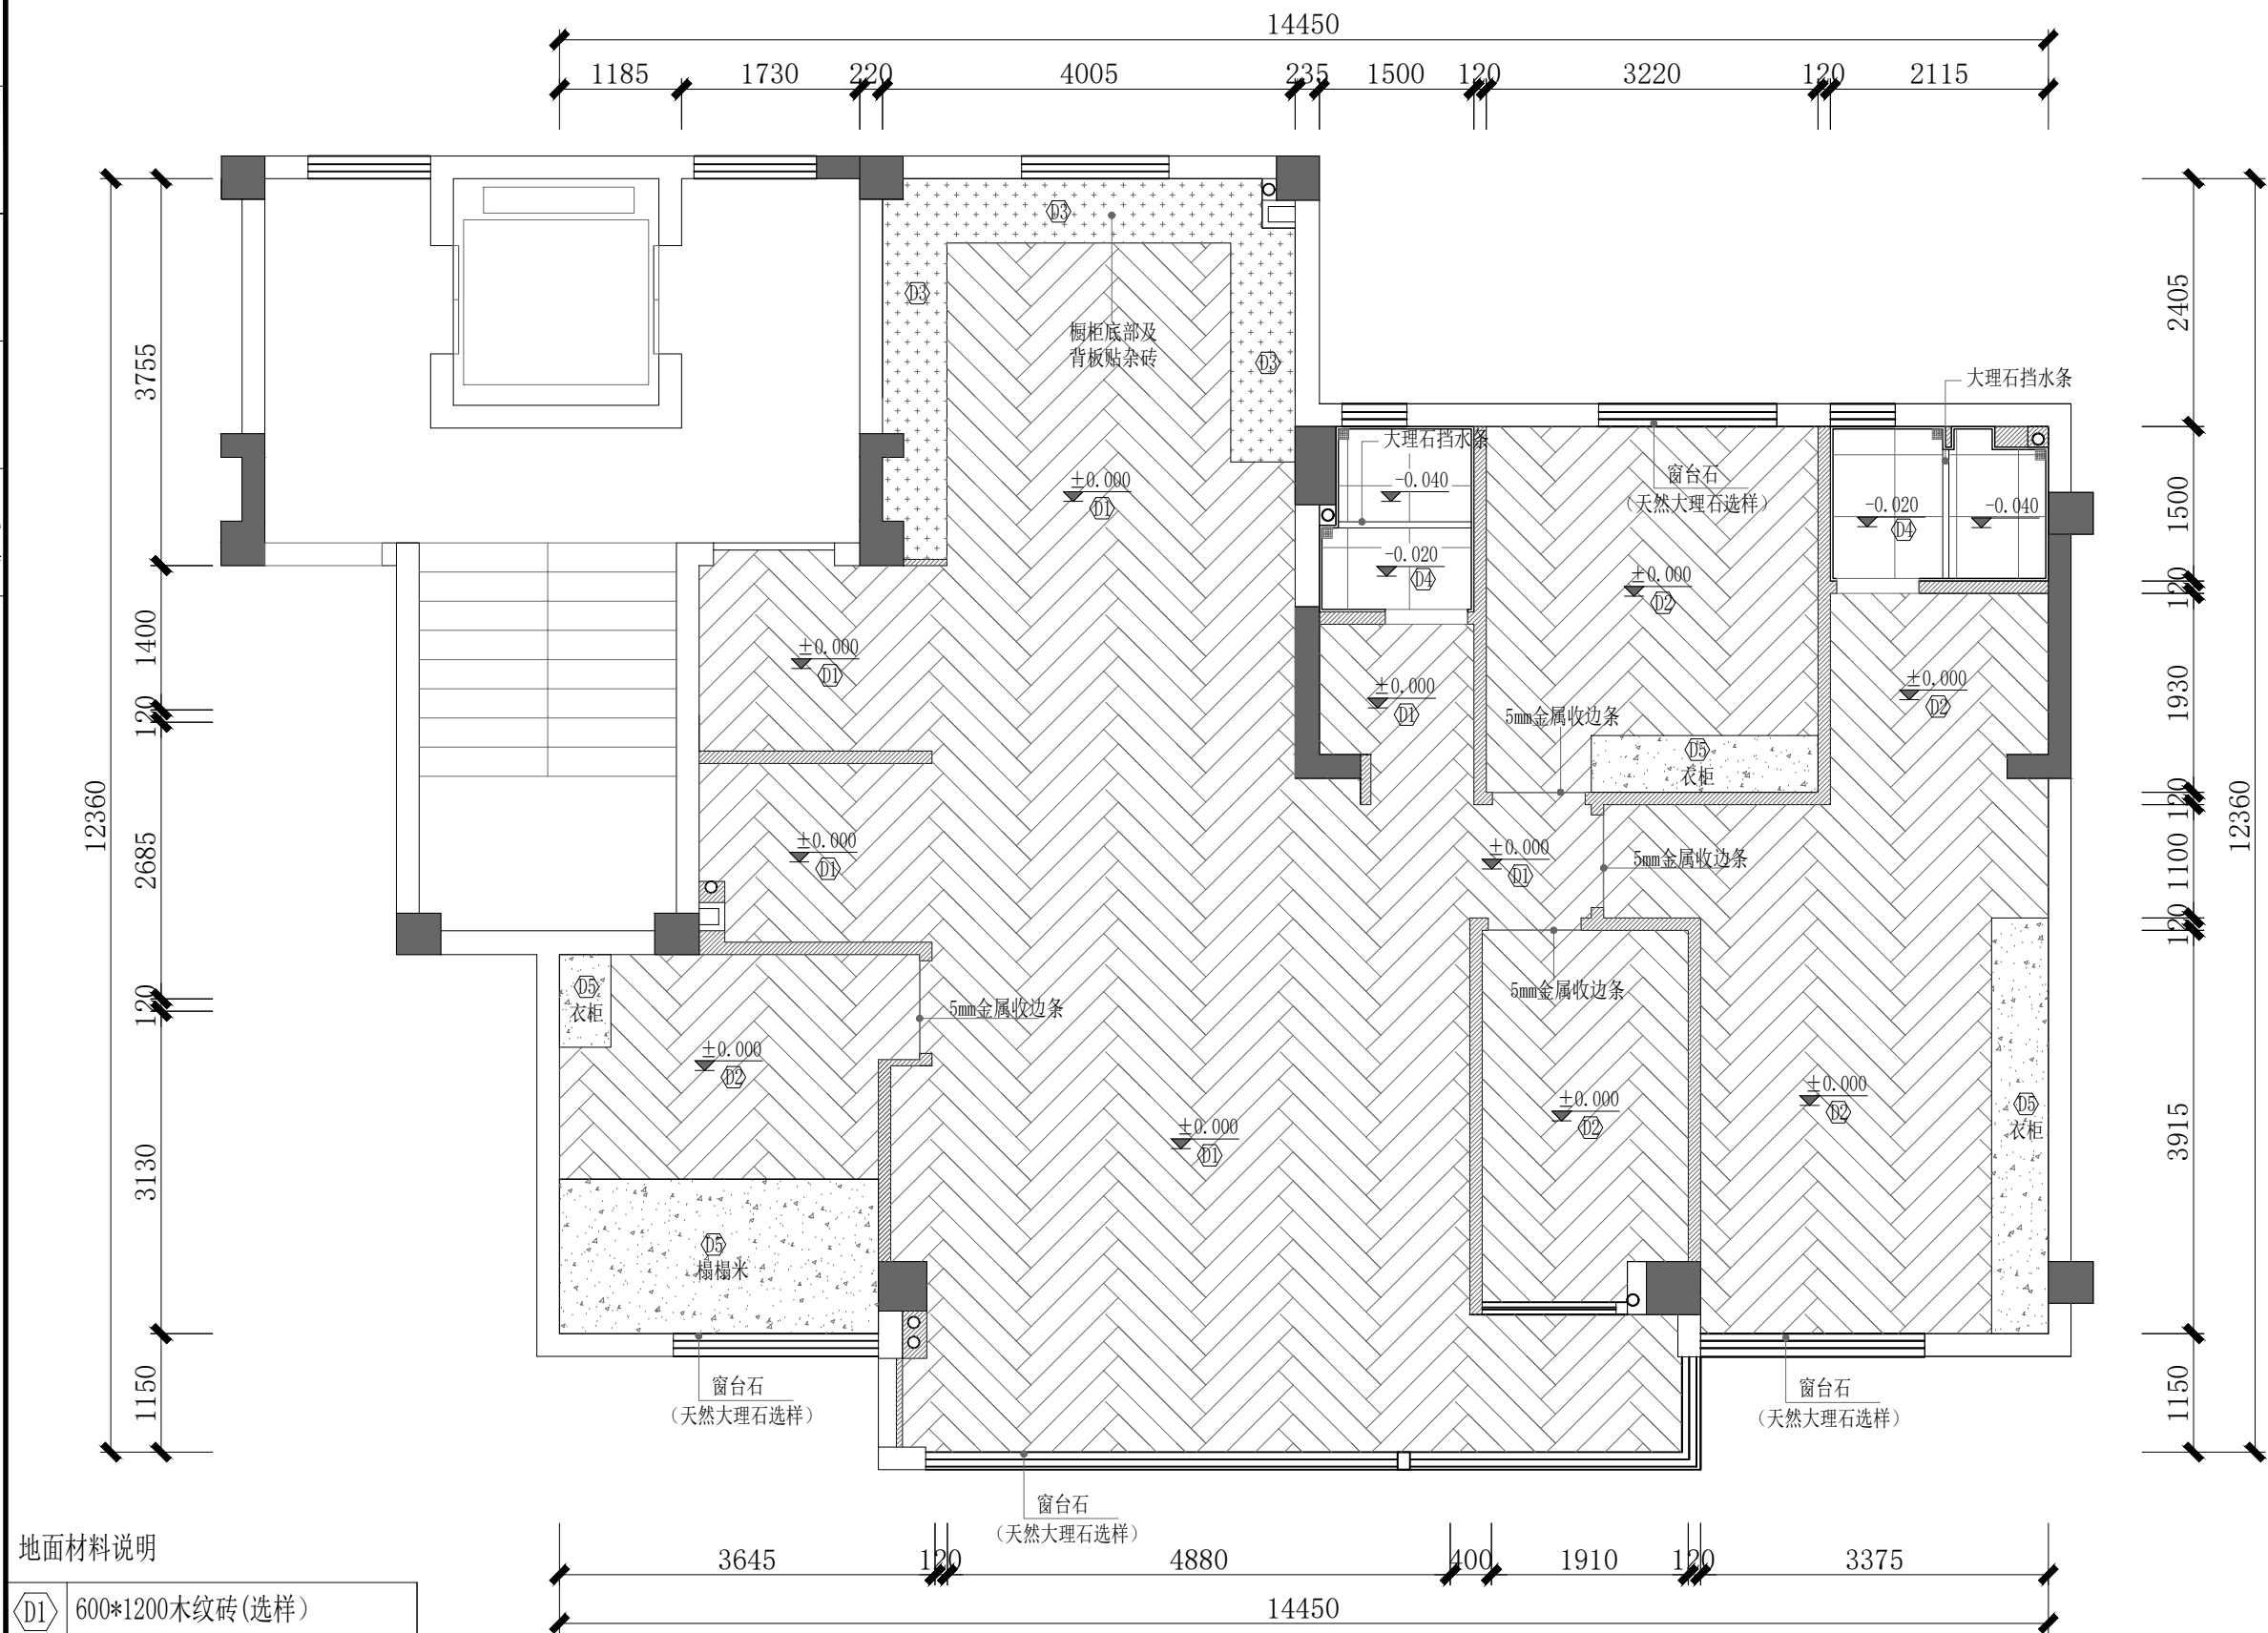

地面材料说明

D1	600*1200木纹砖(选样)
D2	水泥砂浆找平,面铺木地板
D3	杂砖
D4	600*600防滑砖(选样)
D5	柜体底部,水泥砂浆找平

注：除特殊标注外门槛石、窗台石均为天然大理石选样，卫生间门槛石内边水磨45度小斜边。

起铺点


地面材质图 1:50



审 定		
工程负责人		
专业负责人		
审 核		
校 对		
设 计		
制 图		

吊顶布置图

工程编号	
图 别	装 施
图 号	PM-06
日 期	2026/5

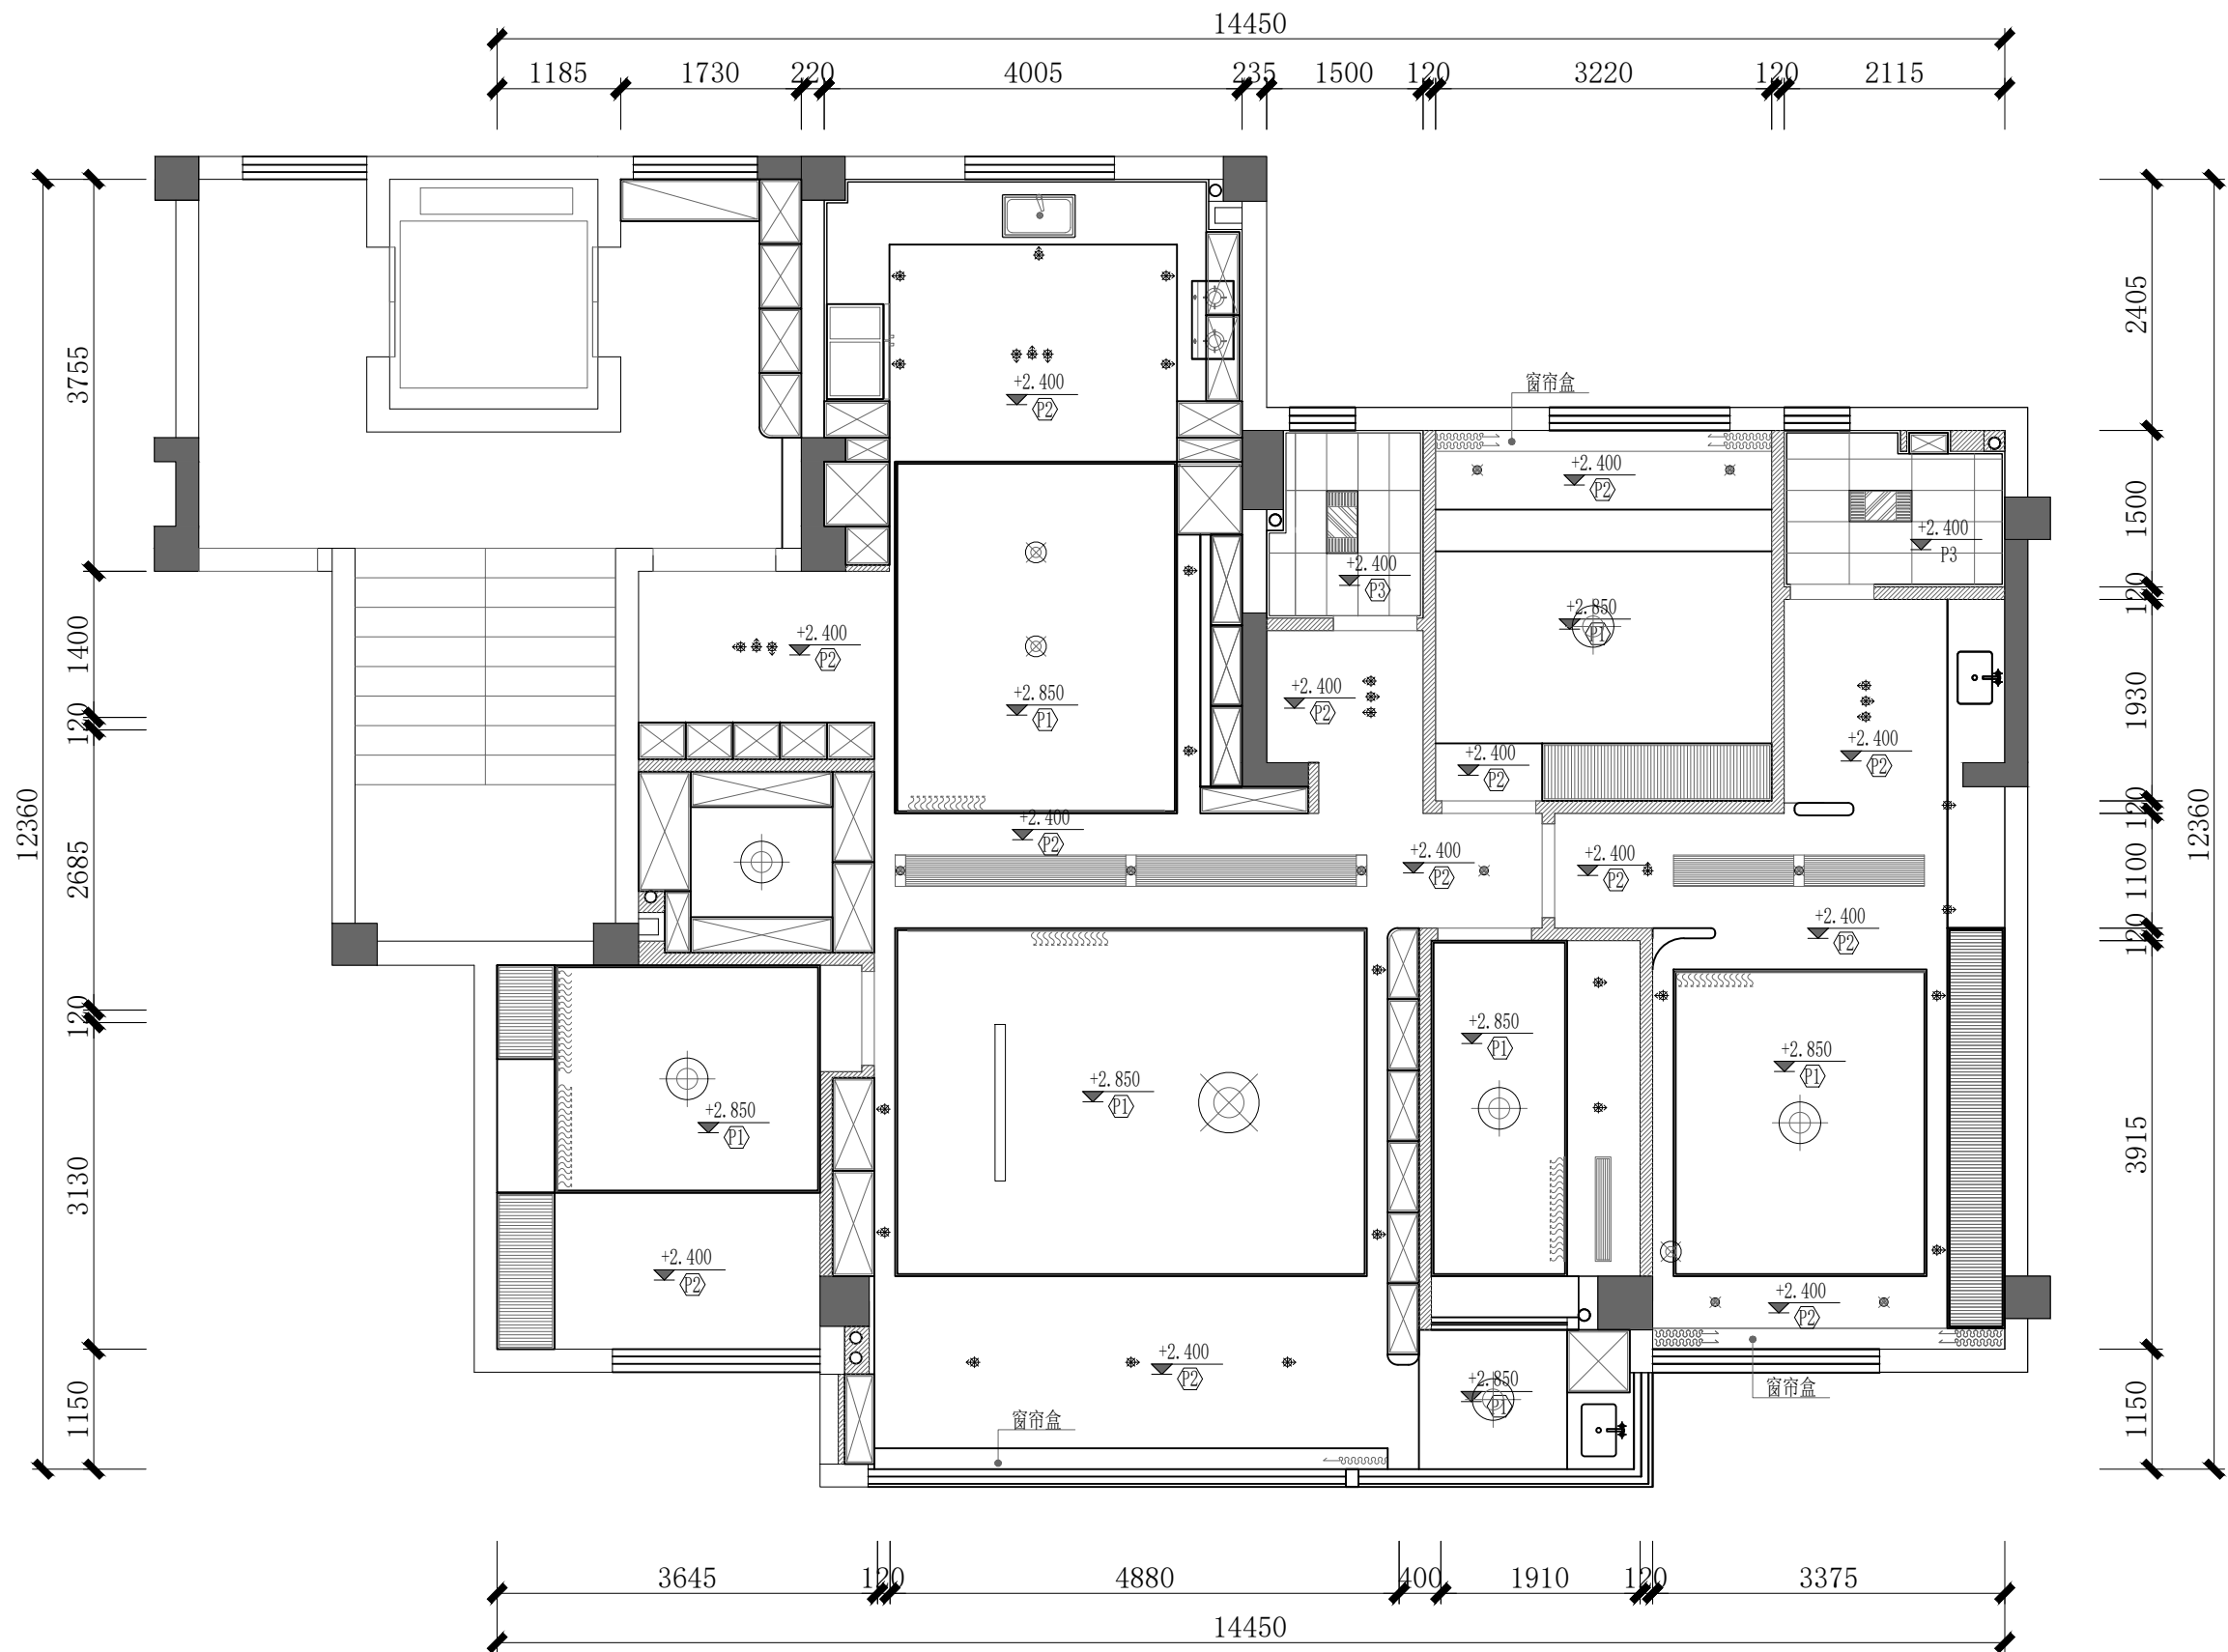

吊顶布置图 1:50

吊顶材料及图例说明

P1	原建筑板底，面饰白色水泥漆								
P2	9mm欧松板底层，面6mm硅酸钙板 面饰白色水泥漆	风暖机	射灯	明装筒灯	明装筒灯	筒灯	防雾筒灯	防雾射灯	风口
P3	集成吊顶								
		定制线型灯		LED灯带	小吊灯	壁灯	轨道灯		吸顶灯



福州·阳光城檀映6#401
室内装饰设计施工图

审 定		
工程负责人		
专业负责人		
审 核		
校 对		
设 计		
制 图		

灯具定位图

工程编号	
图 别	装 施
图 号	PM-08
日 期	2026/5



灯具定位图 1:50

图例说明


							
风暖机	射灯	明装筒灯	明装筒灯	筒灯	防雾筒灯	防雾射灯	风口
							
定制线型灯	LED灯带	小吊灯	壁灯	轨道灯	吸顶灯		



审 定		
工程负责人		
专业负责人		
审 核		
校 对		
设 计		
制 图		

强弱电布置图

工程编号	
图 别	装 施
图 号	PM-09
日 期	2026/5

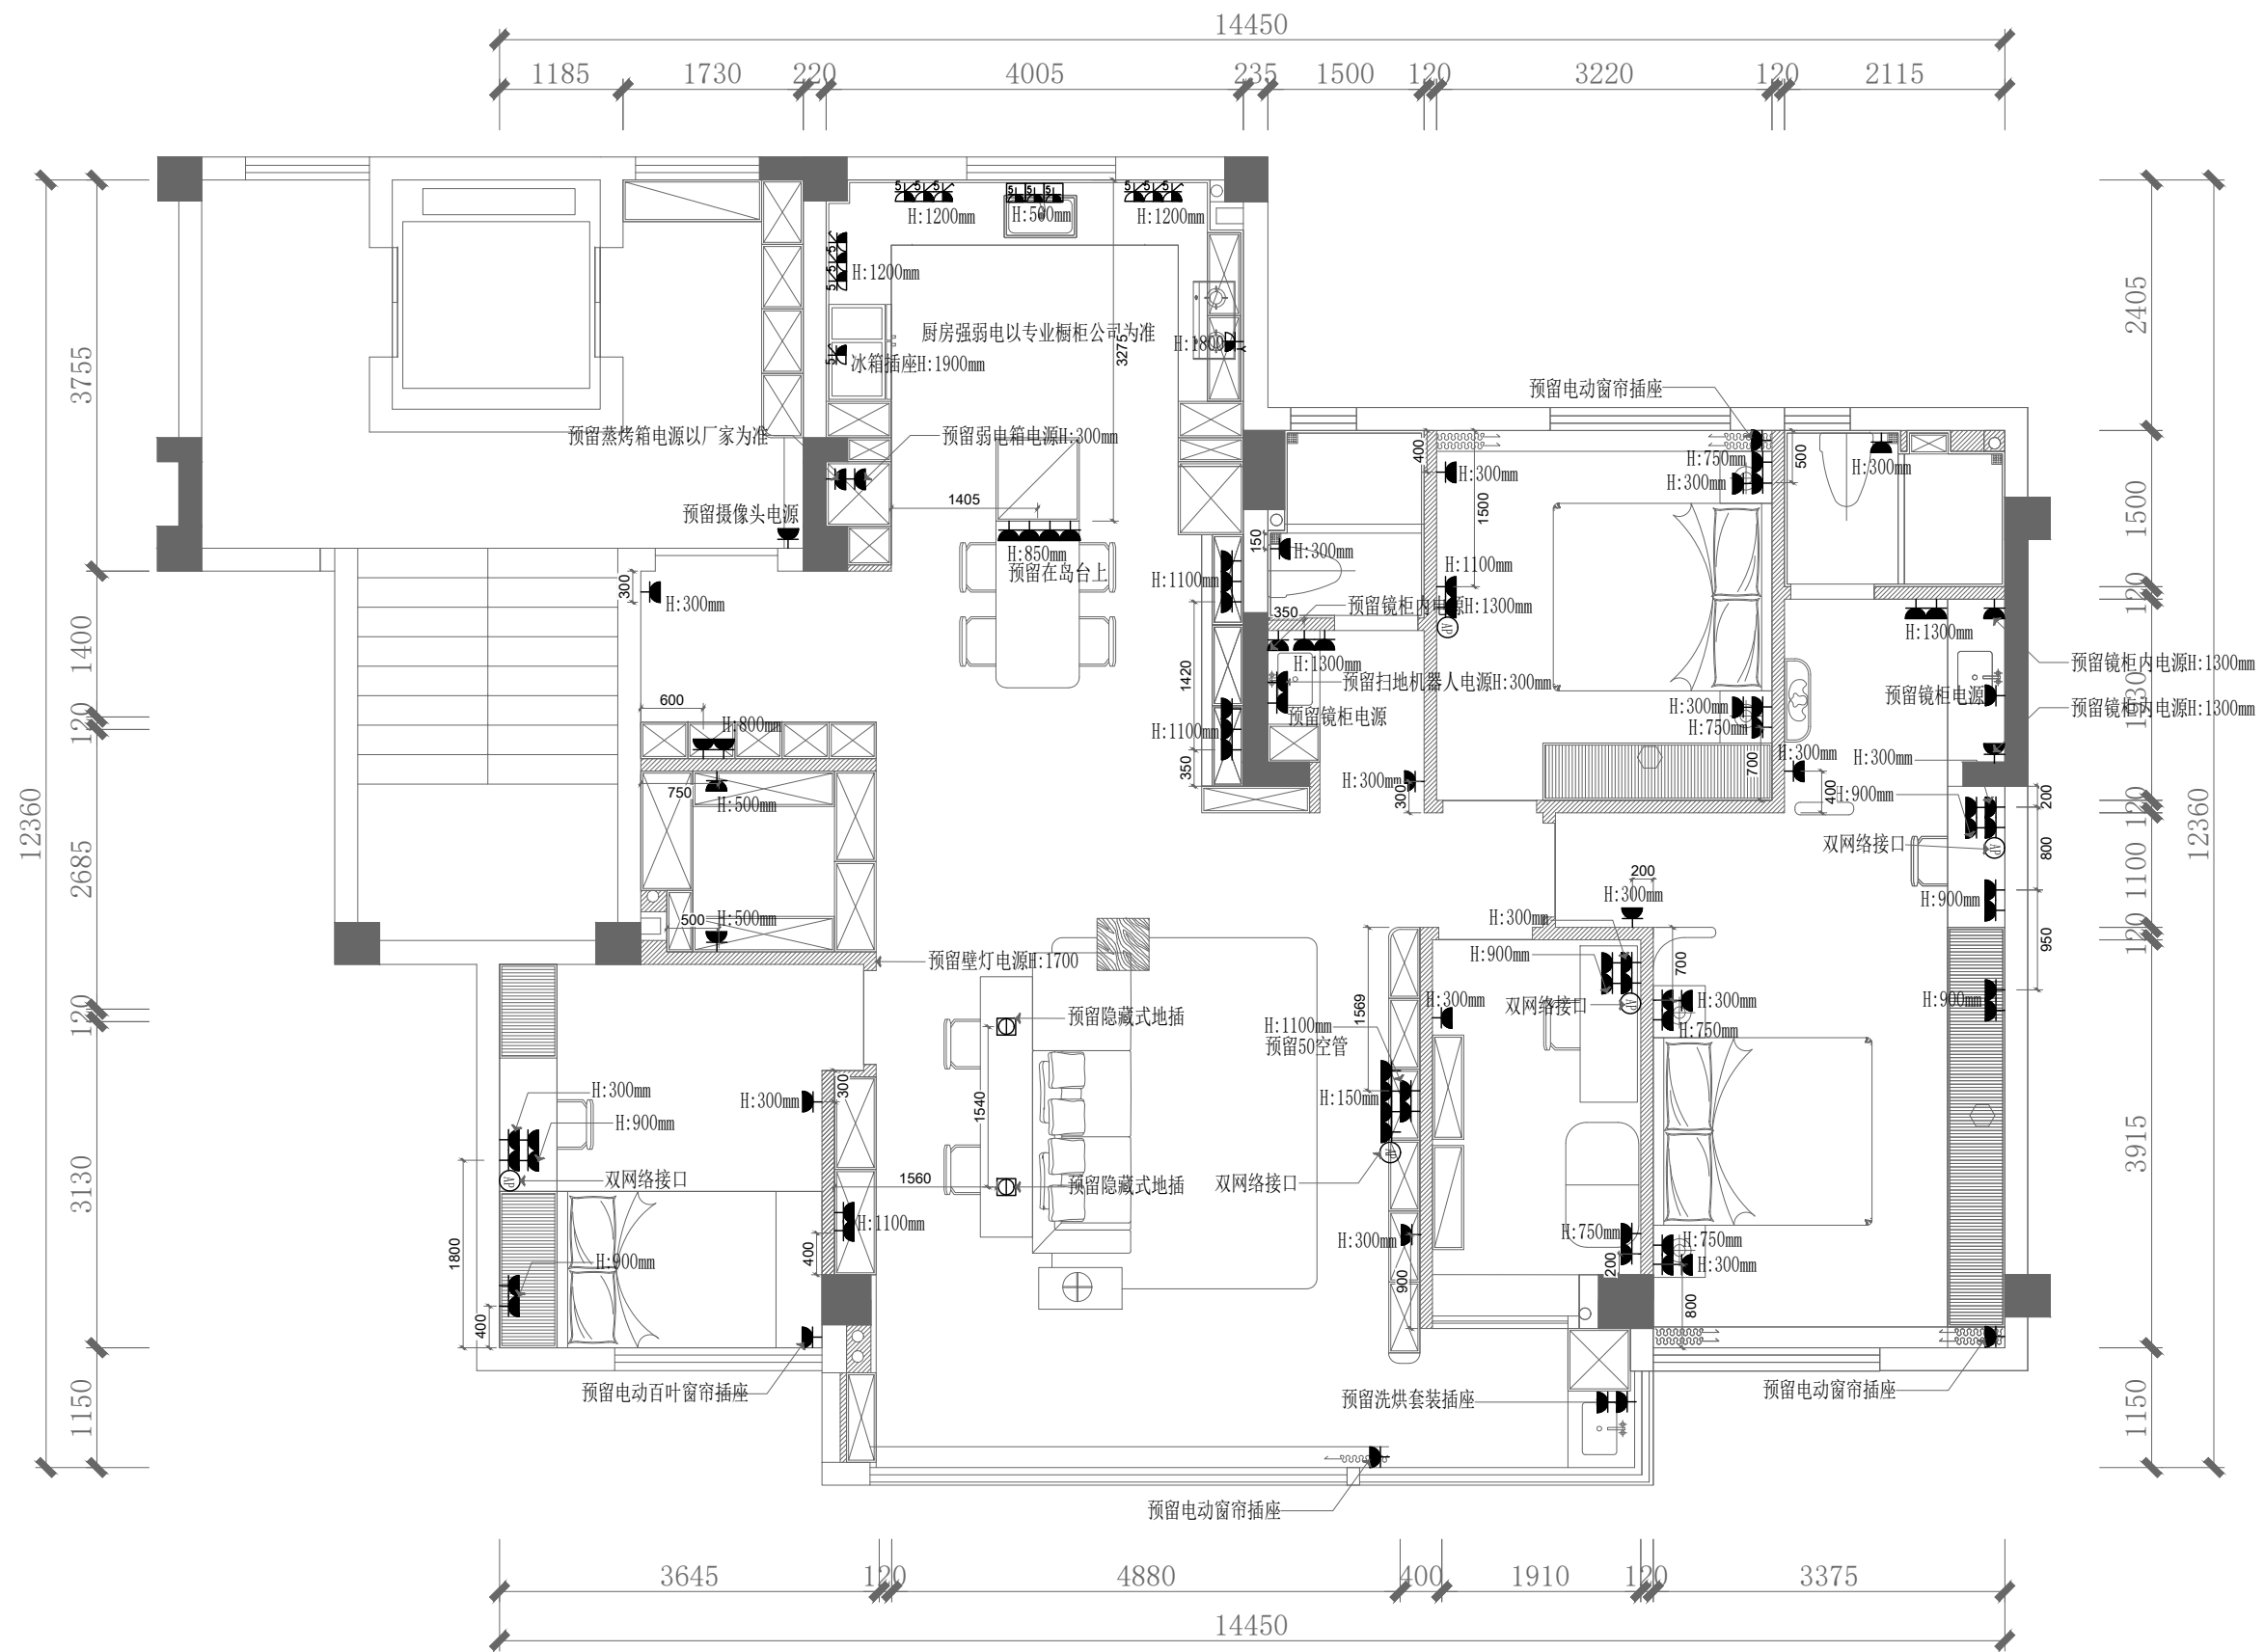

	油烟机插座(带开关)		电视/网络出线盒
	普通五孔插座		热水器防水插座(带开关)
	普通防水插座(带开关)		冰箱插座(带开关)
	带开关空调插座(16A)		网络出线盒
	防静电防尘插座		地面金属插座

注意：此图纸不含音响、监控、新风系统、中央空调、地暖等设备开关插座，如需相关图纸由专业公司配套设计。

强弱电布置图 1:50



福州·阳光城檀映6#401
室内装饰设计施工图

审 定		
工程负责人		
专业负责人		
审 核		
校 对		
设 计		
制 图		

开关控制图

工程编号	
图 别	装 施
图 号	PM-10
日 期	2026/5



单开开关	双开开关	三开开关	四开开关
			
双联单控开关	双联双控开关	双联三控开关	
			

备注：图中无特使标记开关面板高度为1300mm，智能设备以专业公司配套设计为准。

开关控制图 1:50

电	气	图
建	筑	图
结	构	图
水	电	图



单位名称:



艾科装饰
Aike Decoration

备 注:

施工图审查批准单位:

施工图审查批准书证号:

图纸专用章:

注册建筑师执业章:

注册工程师执业章:

工程名称:

福州·阳光城檀映6#401
室内装饰设计施工图

建设单位:

审 定		
工程负责人		
专业负责人		
审 核		
校 对		
设 计		
制 图		

图 名:

家具尺寸图

工程编号	
图 别	装 施
图 号	PM-13
日 期	2026/5

家具尺寸图 1:50



福州·阳光城檀映6#401
室内装饰设计施工图

审 定	
工程负责人	
专业负责人	
审 核	
校 对	
设 计	
制 图	



立面索引图

工程编号	
图 别	装 施
图 号	PM-14
日 期	2026/5



立面索引图 1:50

发	电				
包	气				
工	费				
长	有				

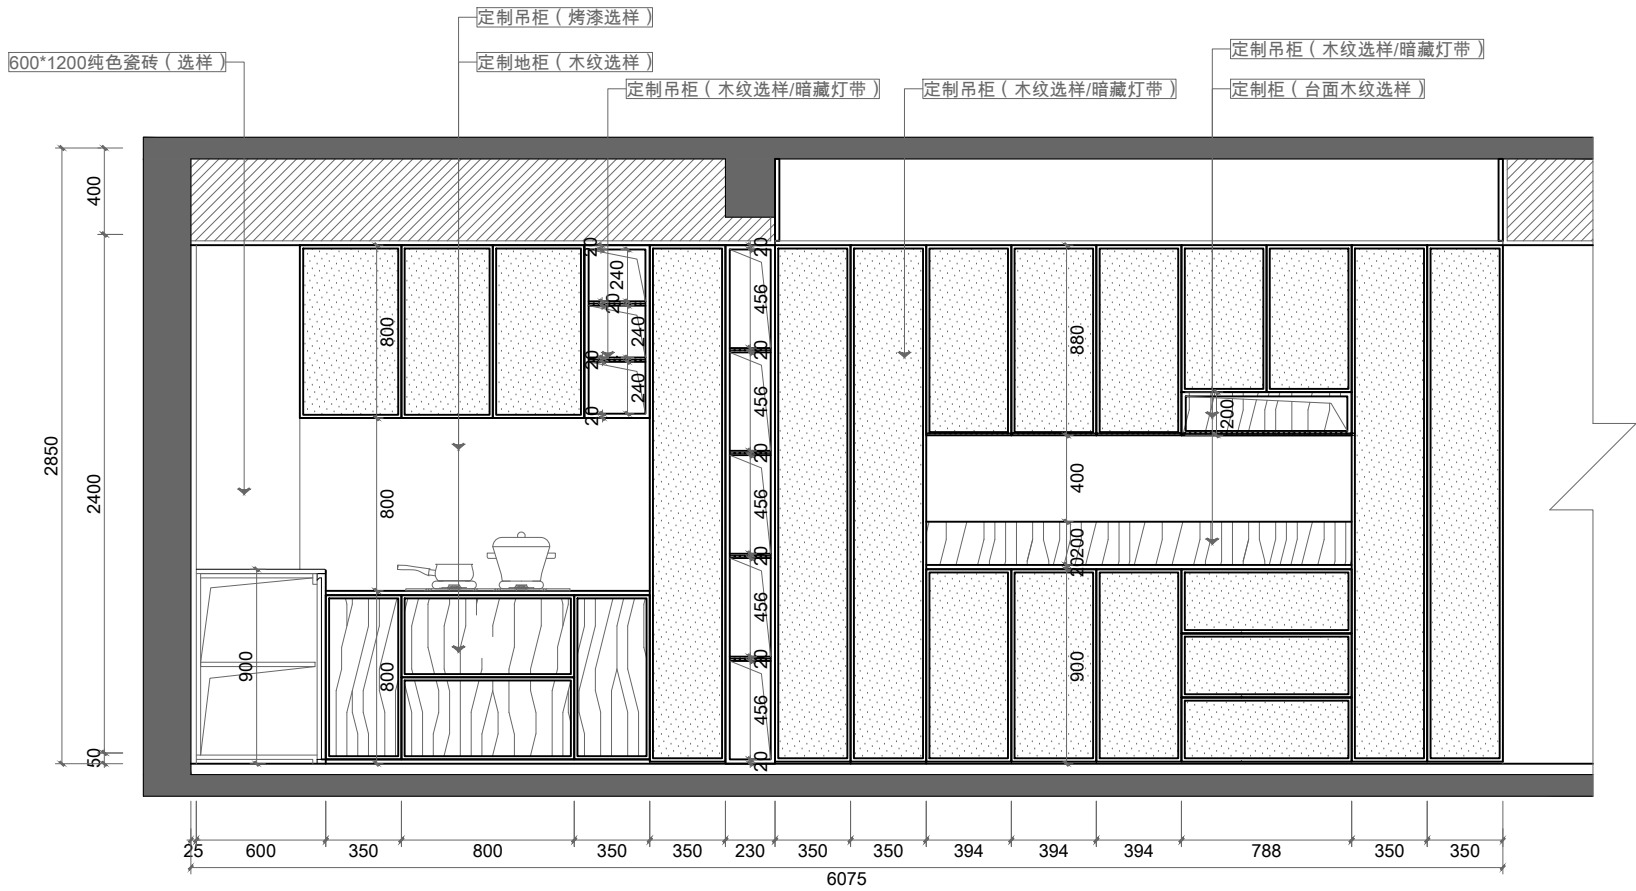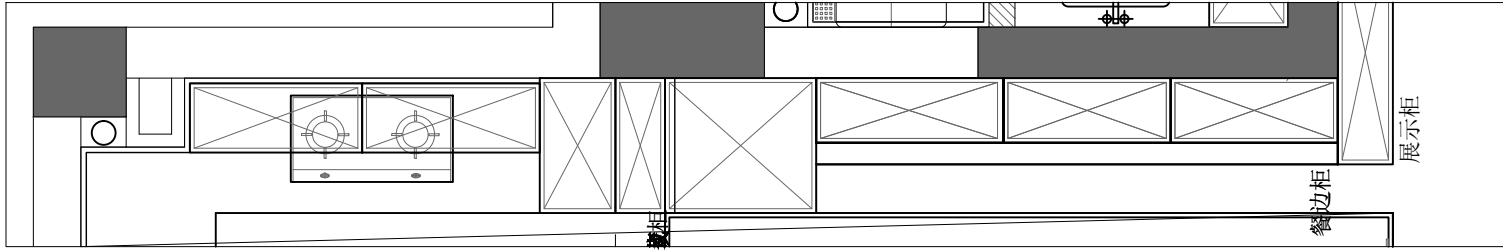




B 厨房、餐厅B立面图 1:35

单位名称：		
		
备 注：		
施工图审查批准单位：		
施工图审查批准证书号：		
图纸专用章：		
注册建筑师执业章：		
注册工程师执业章：		
工程名称： 阳光城檀映6#401		
建设单位：		
审 定		
工程负责人		
专业负责人		
审 核		
校 对		
设 计		
制 图		
图 名：		
厨房、餐厅B立面图		
工程编号		
图 别	装 施	
图 号	LM-03	
日 期	2026/05	




干区D立面图
干区B立面图

工程编号	
图 别	装 施
图 号	LM-07
日 期	2026/05

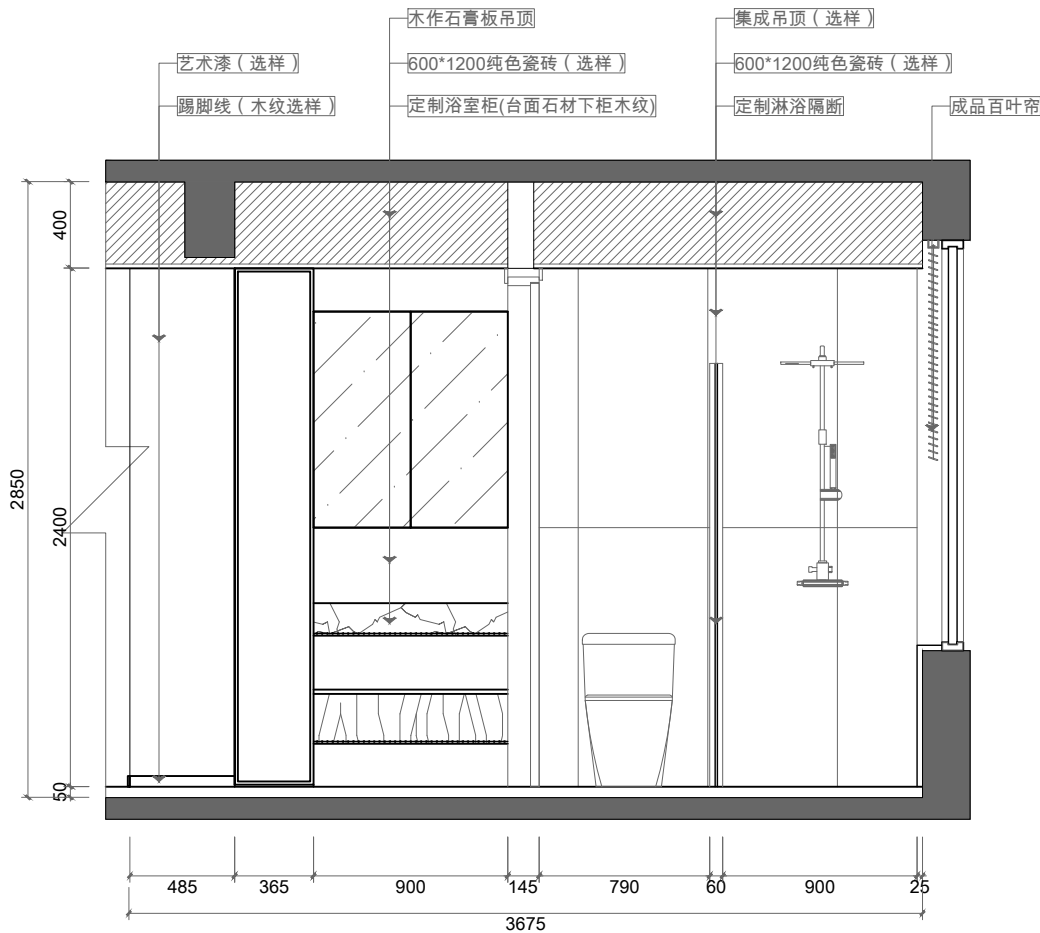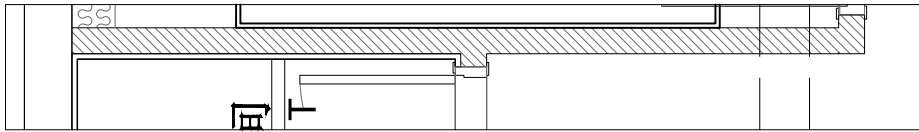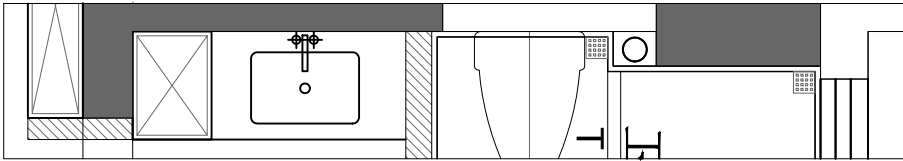

干区D立面图 1:35

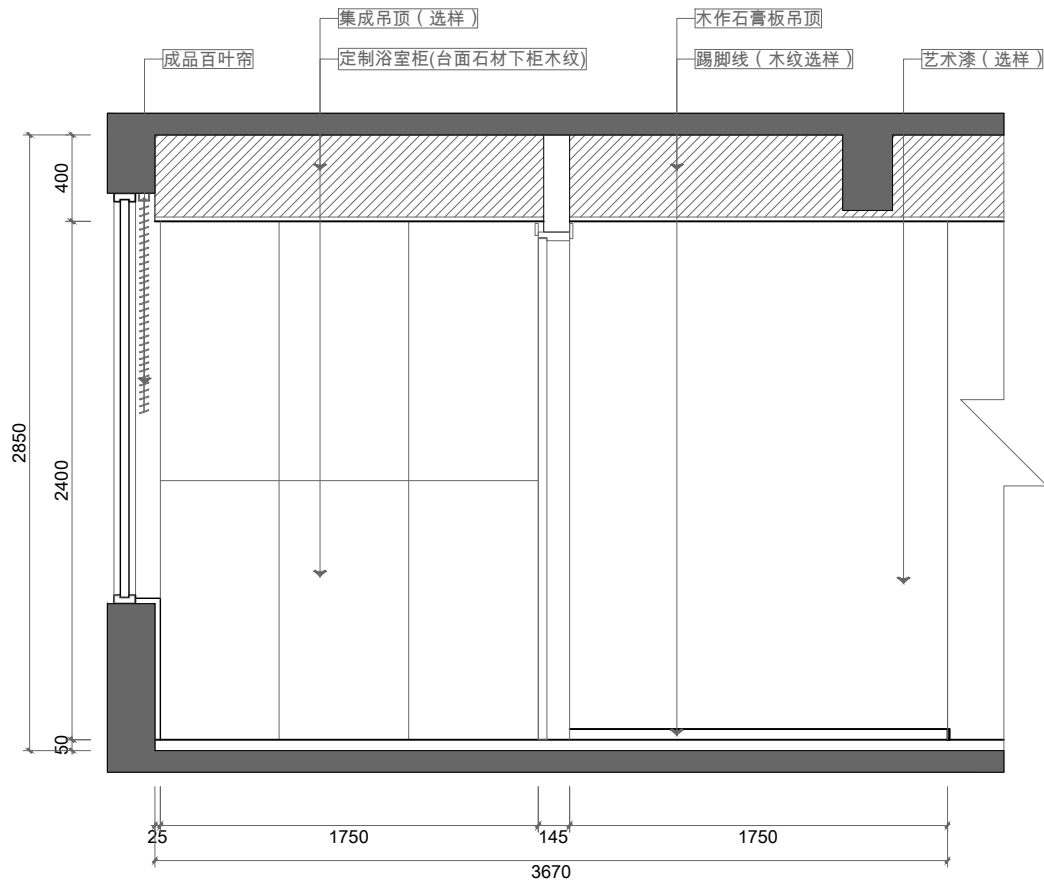




干区B立面图 1:35




阳光城檀映6#401

书房A立面图

2026/05

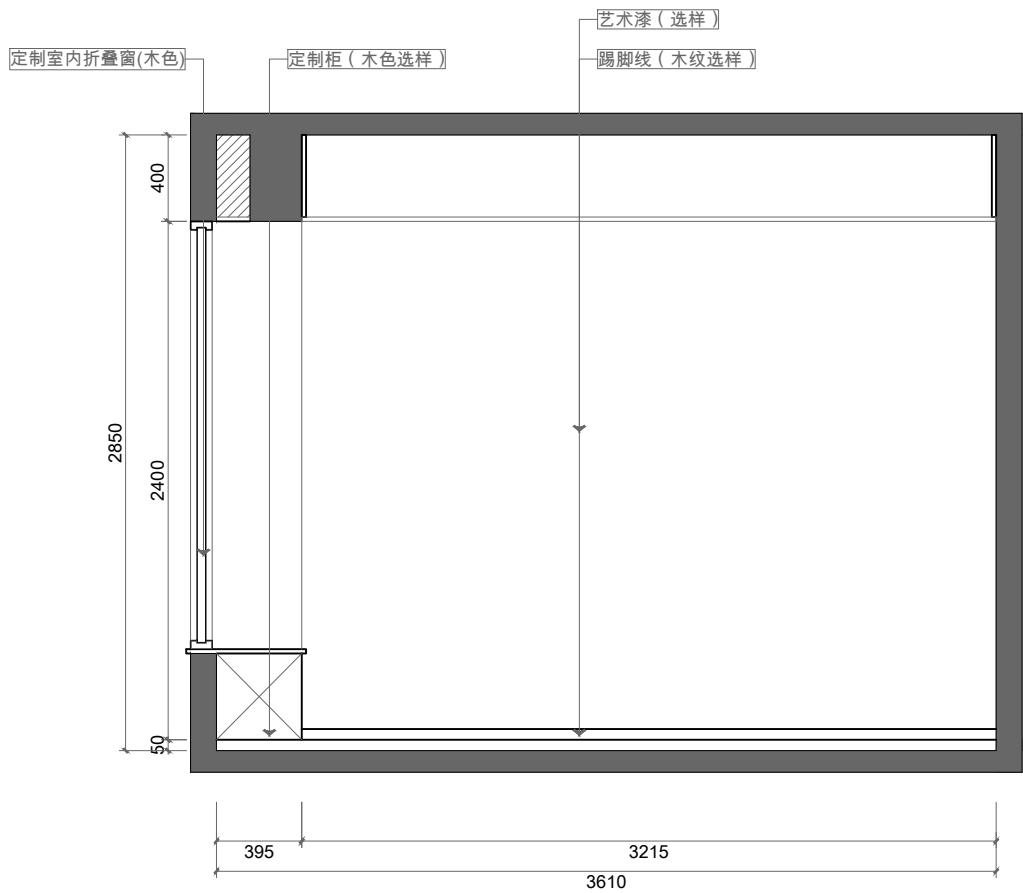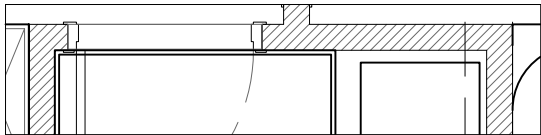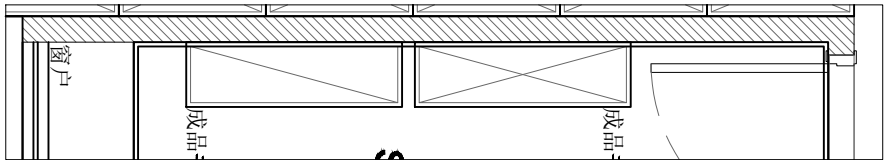

书房D立面图 1:35

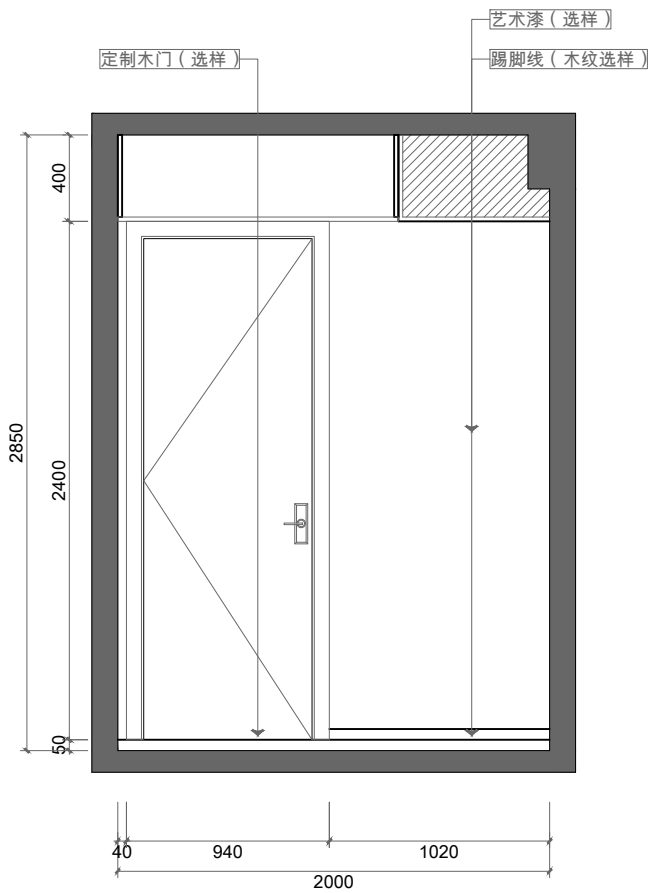




书房A立面图 1:35




审 定		
工程负责人		
专业负责人		
审 核		
校 对		
设 计		
制 图		

主卧A立面图
主卧干区、主卫D立面图

工程编号	
图 别	装 施
图 号	LM-13
日 期	2026/05

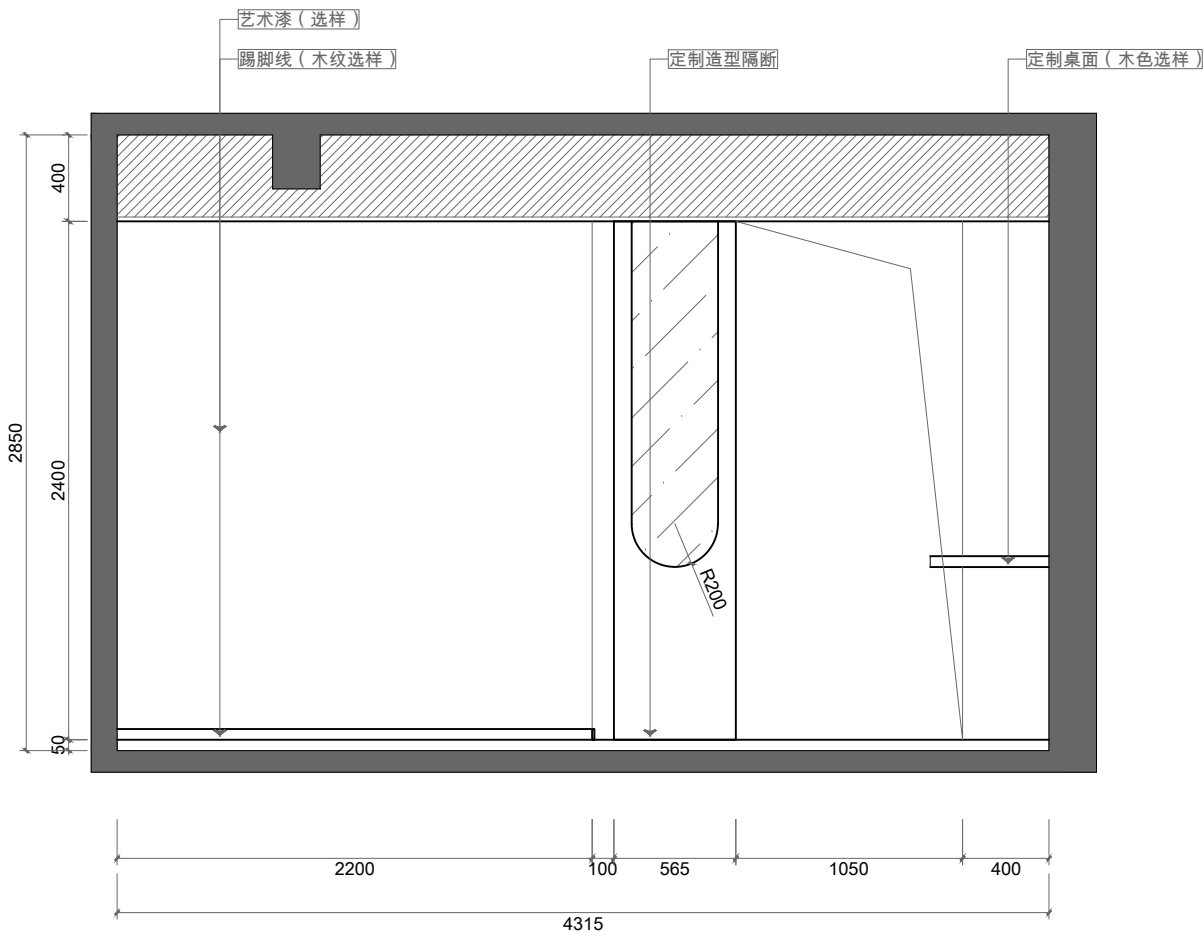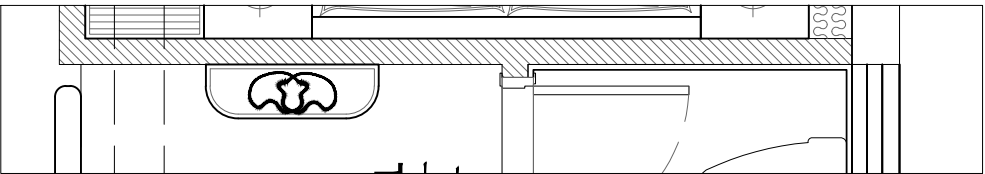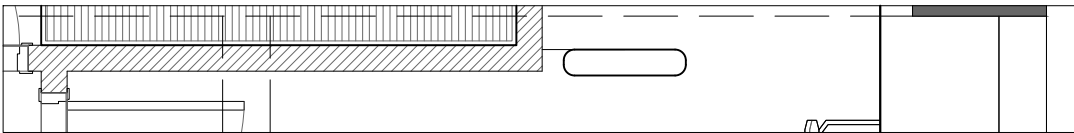

主卧室A立面图 1:35

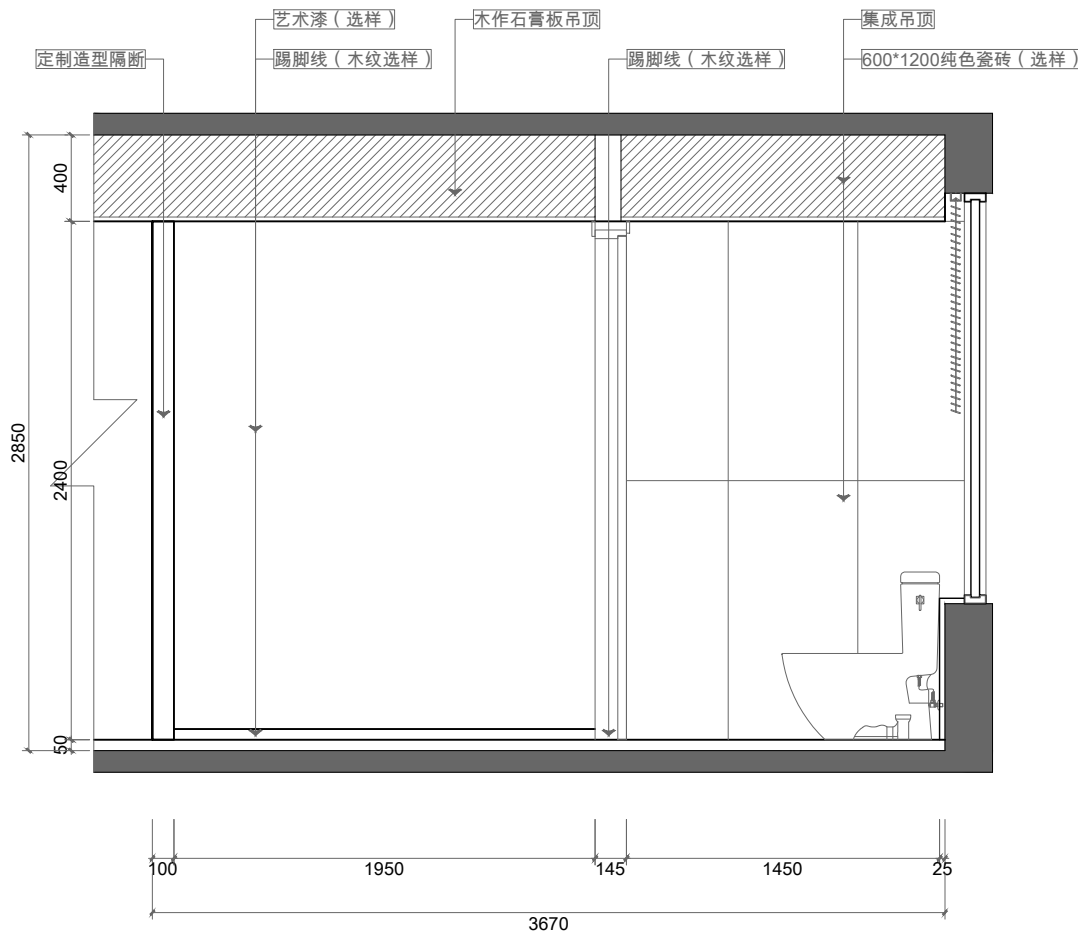




主卧室干区、主卫D立面图 1:35




阳光城檀映6#401

主卧室C立面图

2026/05

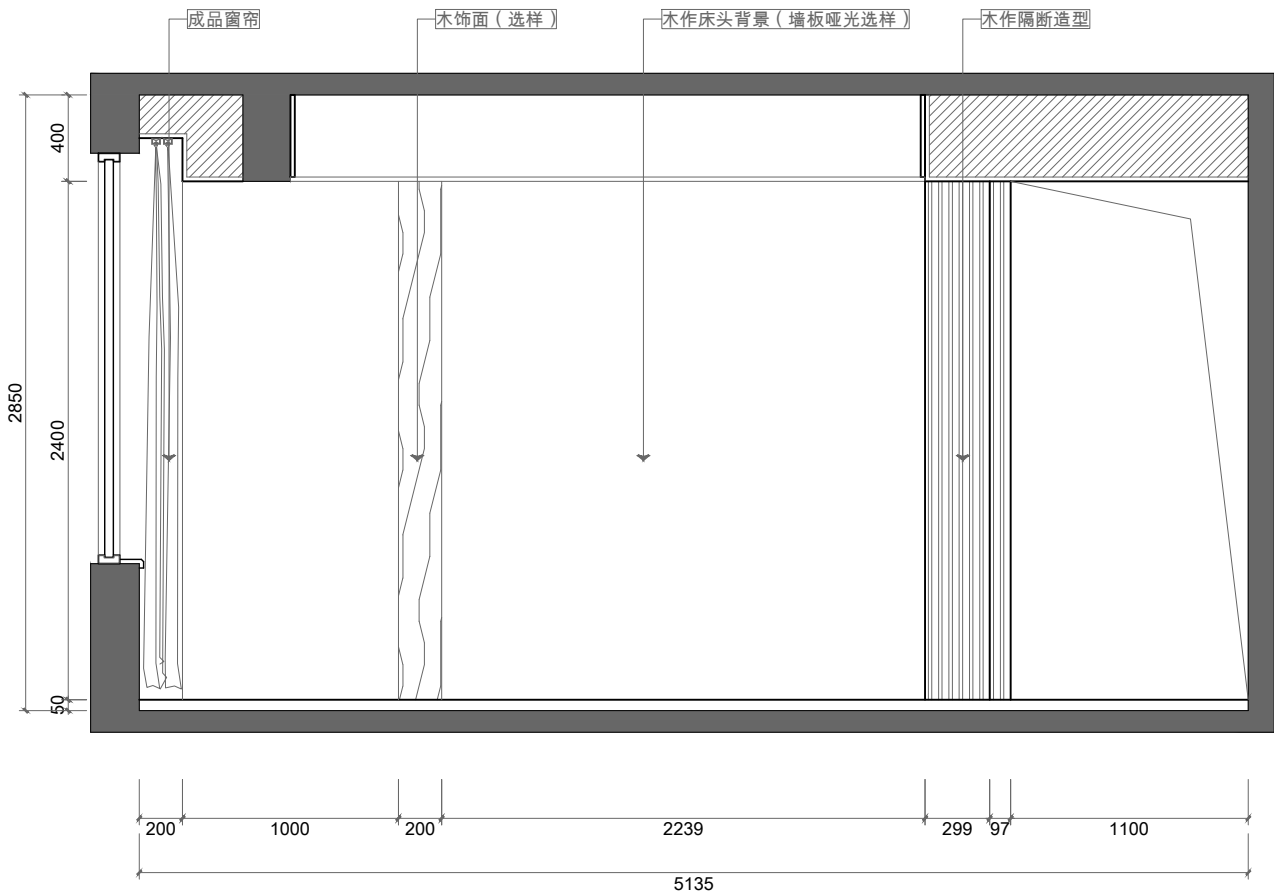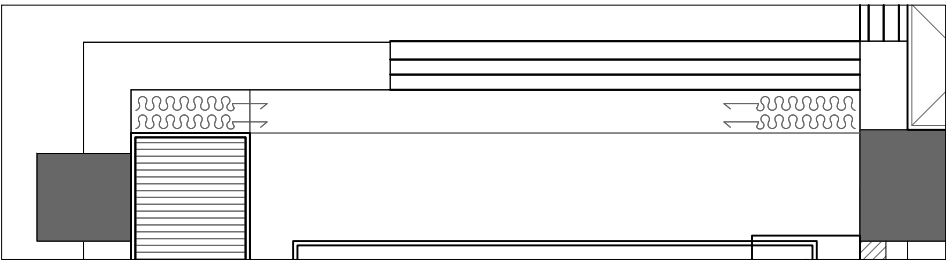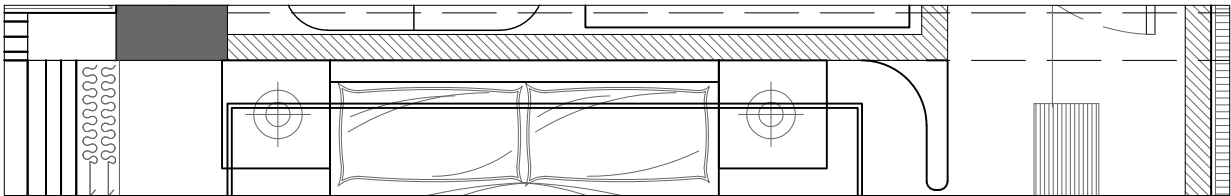


 主卧D立面图
 1:35

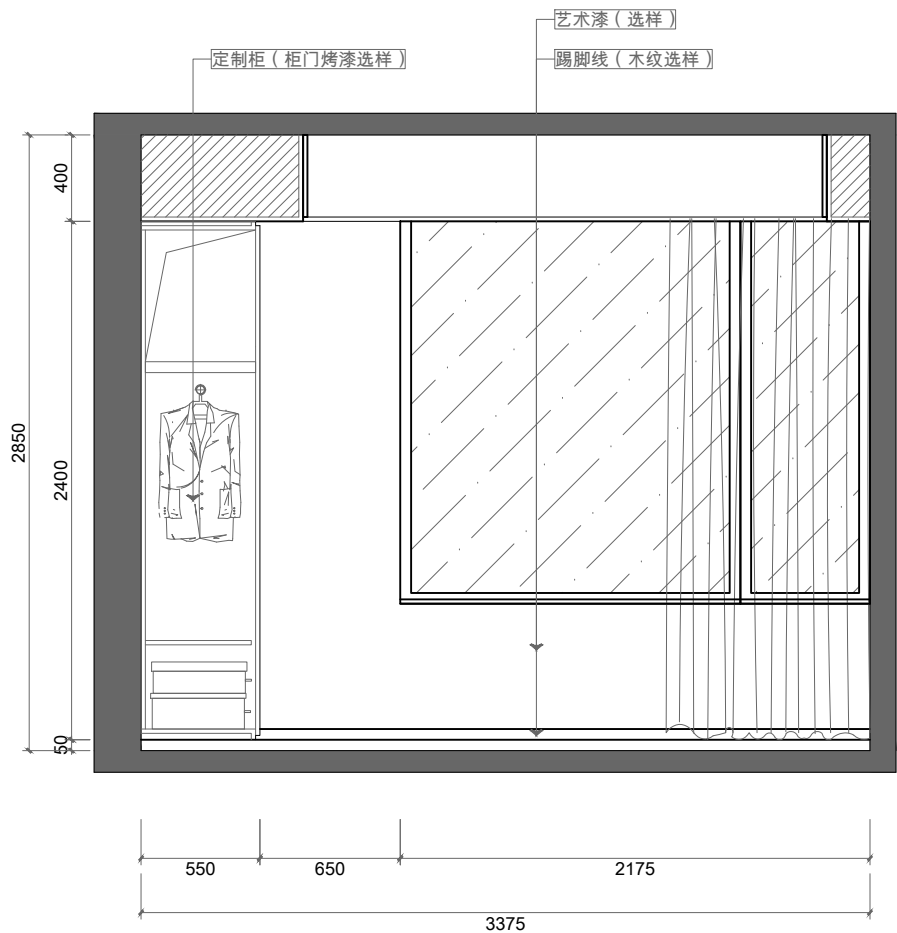

主臥C立面图 1:35

